

DEVIS N° 50588-1-A
btu

24/03/2026

ENTECH

11 ALLEE JEAN FRANCOIS DE LA PEROUSE
29000 QUIMPER

EXINCODIS-OMBRIERES

Ombrière sur parc au sol

4 Rue Philippe Goudey 25400 EXINCOURT

Indice	Date	Commentaire
A	24/03/2026	Origine

Contact : TUPINON Benoit | Responsable Cellule Ombrières | 06 29 47 64 68 | b.tupinon@briand.fr

BRIAND CONSTRUCTION METALLIQUE | « le campus » | 69800 Saint Priest | Tél : 04 78 70 80 49
SAS au capital de 2 640 000 € | N° SIRET : 308 575 158 000 24 | CODE NAF : 4120 B | N° TVA INTRACOMMUNAUTAIRE : FR 69 308 575 158

Ce document confidentiel est la propriété de BRIAND CONSTRUCTION METALLIQUE. Toute communication à des tiers doit faire l'objet d'un accord écrit de sa part.

Description	Total
<u>OMBRIERE P.V.</u>	
Ossature métallique ombrière galvanisée	548 833,54 €
Support onduleurs	486,00 €
Protection périphérique des poteaux	10 944,00 €
Capotage des descentes de câble	1 177,02 €
Liaison non structurelle entre ombrière	1 265,00 €
Gestion des E.P.	74 187,20 €
Fourniture du système d'intégration	135 979,30 €
Pose du SI et des panneaux	91 397,57 €
Total H.T.	864 269,63 €
T.V.A. (20%)	172 853,93 €
TOTAL T.T.C.	1 037 123,56 €

Mois d'établissement des prix : mars 2026

Durée de validité du devis : 30 jours à compter de la date d'émission.

CONDITIONS ADMINISTRATIVES PARTICULIERES : Notre offre est basée sur les conditions administratives de la norme NFP 03 001 notamment pour les pénalités de retard : montant 1/3000 par jour calendrier plafonnées à 5% de notre marché et libératoire de tout préjudice.

CONDITIONS DE PAIEMENT : sur facture à 30 jours fin de mois. Ce paiement s'entend sans aucune déduction pour escompte ou pour retenue de garantie.

% du prix	Échéances de facturation
15 %	Signature du Contrat / Emission de la commande ou du contrat de sous-traitance
75 %	Selon avancement de chantier
5 %	A la signature du PV de réception
5 %	A la levée des réserves, et au plus tard au parfait achèvement, cautionnable

MODES DE PAIEMENT : Paiement par virement bancaire ou par chèque.

PRORATA : Il n'est pas prévu de frais de compte prorata

Responsabilité élargie du producteur (REP Bâtiment) :

Eco-organisme : VALOBAT

N°IDU : FR308176_04KMFP

La part du coût unitaire que BRIAND supporte pour la gestion des déchets de PMCB, tel que facturé par l'éco-organisme auquel BRIAND adhère, est intégralement répercutée à l'acheteur professionnel du produit sans possibilité de réfaction.

NOTA :

Nos prix sont établis pour une exécution des travaux sur chantier en une seule intervention. Dans le cas d'interventions multiples sur site, non prévues au marché, les coûts liés aux rapatriements de personnel, aux transports supplémentaires et au matériel de chantier vous seront répercutés.

Les prix sont révisibles et il sera fait application de la formule d'actualisation des prix suivante :

Prix actualisé = (Prix devis) x (indice BT du mois d'intervention sur site) / (indice BT du mois d'établissement des prix).

(L'indice est à définir en fonction de la nature des travaux. Ex: BT07 pour la charpente métallique, les bardages et couvertures en acier)



LES HERBIERS
LYON
AIX-EN-PROVENCE
LILLE



Les Herbiers (85) | Lyon (69)
Aix-en-Provence (13) | Lille (59)

Le spécialiste de la construction métallique

Depuis plus de 70 ans, BRIAND Métal porté par la société Briand Construction Métallique, intègre tous les savoir-faire en matière de construction métallique, de la conception à la fabrication et au montage de bâtiment, des plus simples aux plus complexes.

Pour construire toujours plus durablement et décarboné, BRIAND Métal propose des solutions innovantes associant le bon matériau au bon endroit en mixant le métal au bois et au béton.

- charpente métallique
- bardage et façade
- couverture
- serrurerie industrielle

Pour tous types de bâtiments : bâtiment commercial, industriel, logistique, tertiaire, culturel ou sportif, parking aérien, logement résidentiel, ...

En 2024 :

- 100M€ chiffre d'affaires
- 270 collaborateurs
- 74 ingénieurs et techniciens
- 1 sites de production
- 20 000 tonnes d'acier usinées par an



Parking aérien Monge
Dijon (21)



Le Colisée
Chartres (28)



Airbus beluga
Blagnac (31)

La présentation de BRIAND – METAL, BOIS, BETON



Construire toujours mieux, ensemble

Leader de la construction métallique de bâtiments, nous nous appuyons sur un collectif de savoir-faire multi-matériaux et filiales d'excellence pour proposer des techniques et solutions innovantes, sur-mesure ou standardisées.

À la fois concepteur, constructeur et industriel, nous garantissons la qualité au juste prix, du lot séparé au tous corps d'état, dans des délais et coûts optimisés, au travers d'une approche collaborative, responsable et respectueuse des femmes, des hommes et de la planète.

NOS SAVOIRS-FAIRE

01. Structures & enveloppes

02. Rénovation & transformation

03. Parkings & mobilités

04. Offre globale

05. Performance énergétique

290 M€
chiffre d'affaires

1030
collaborateurs

14
implantations

800
Chantiers/an

NOTRE APPROCHE POUR UNE CONSTRUCTION PLUS DURABLE



Optimisation des structures pour réduire la quantité de matériaux



Métal, bois, béton : le bon matériau au bon endroit pour plus de sobriété



Recours massif à la préfabrication pour plus de circularité dans nos constructions



Plusieurs expériences réussies en rénovation d'ouvrages



L'analyse du cycle de vie des projets intégrée dès l'offre de prix



Des solutions concrètes de constructions réversibles conçues pour le réemploi


1. Caractéristiques du projet (OMBRIERE)

Fourniture et pose d'ossatures support d'ombrières PV dont les caractéristiques sont les suivantes :

- Ossature : ancrage en pied de poteau (fourniture au gros œuvre pour implantation).
 - : portiques PRS mono poteau encastrés en pied
 - : portique PRS multi-poteaux articulés en pied dans le cas des ombrières liaisonnées
 - : traverse, bracon et panne PLS en profils galvanisés formés à froid (ép. panne 15/10 mini)
 - : Stabilité transversale et longitudinale assurée par l'encastrement des poteaux en pied
 - : Stabilité transversale assurée par l'encastrement des traverse sur les poteaux dans le cas des ombrières liaisonnées
 - : Stabilité longitudinale assurée par croix de stabilité située dans une travée
- Dimensions : selon plans joints
- Hauteur faitage dessus fer : selon plans joints
- Hauteur libre sous traverse : selon plans joints
- Hauteur libre sous bracon : selon plans joints
- Pente : selon plans joints
- Entraxe poteau : selon plans joints
- Niveau de pose des poteaux : -0,30m pour tous les poteaux (les ancrages et raidisseurs éventuels en pied de poteaux resteront visibles).
- Niveau fini sur la voirie finie : variable. L'ombrière suivra la pente moyenne éventuelle du terrain
- L'ensemble de la structure est prévu galvanisé (par procédé sendzimir Z275 pour les profils formés à froids PLS. Galvanisation à chaud 70μ mini pour le reste de la charpente). Il n'est pas prévu dans notre offre de peinture de finition ni de thermolaquage.
- Aucune protection au feu n'est prévue dans notre offre.
- La pose de l'ensemble des ombrières est prévue en une intervention par phase (4 phases de prévues).

Fourniture et pose d'éléments secondaires suivants:

- protections en pied de poteaux; composées de deux arceaux métallique galvanisés et boulonnés sur le poteau:

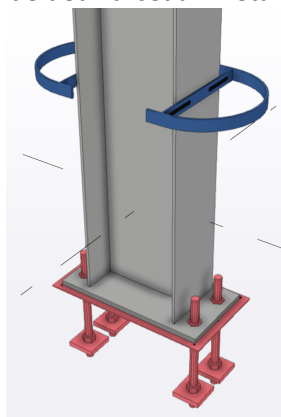

- capotage des descentes de câbles par mise en place d'une tôle acier galvanisée sur une face, sur la hauteur d'un poteau
- support onduleurs, réalisés en profilés minces formés à froid; galvanisation Z275, fixé en tête de poteau.
- liaisons non structurelles entre ombrières, réalisées en profilés minces formés à froid; galvanisation Z275, fixées de traverses à traverses.

Pose de gouttière, compris descentes d'eau pluviale jusqu'au niveau +0,00m (coude en pied pour renvoyer l'eau sur le bitume) comprenant :

- Une cornière de reprise de gouttière fixée en bout de rail.
- Une dalle aluminium, compris fonds, naissances, et descentes.
- La pose des gouttières est prévue en une intervention par phase.

Fourniture du système d'intégration du type JORIS RSPark. Fixation sur les pannes par boulons en fond de rail du système d'intégration.




Pose du système d'intégration et pose seule des panneaux photovoltaïques comprenant :

- La pose de 8983 ml de rail.
- La pose de 4909 unités de panneaux de dimensions 1,762m x 1,134m.
- La pose du système d'intégration et des panneaux sont prévus en une seule intervention par phase.

Non compris :

- Tout travaux d'installation et de raccordement électrique (pose d'onduleurs, raccordement entre panneaux, ...).
- Les travaux de VRD et de GO.
- Le relevé géomètre du parking existant.
- La fourniture des panneaux.
- Le raccordement de l'attente EP et la descente EP est à prévoir par le lot GO ou VRD après la mise en œuvre de la descente EP.
- Toutes prestation non décrite dans ce présent document.

2. Planning prévisionnel

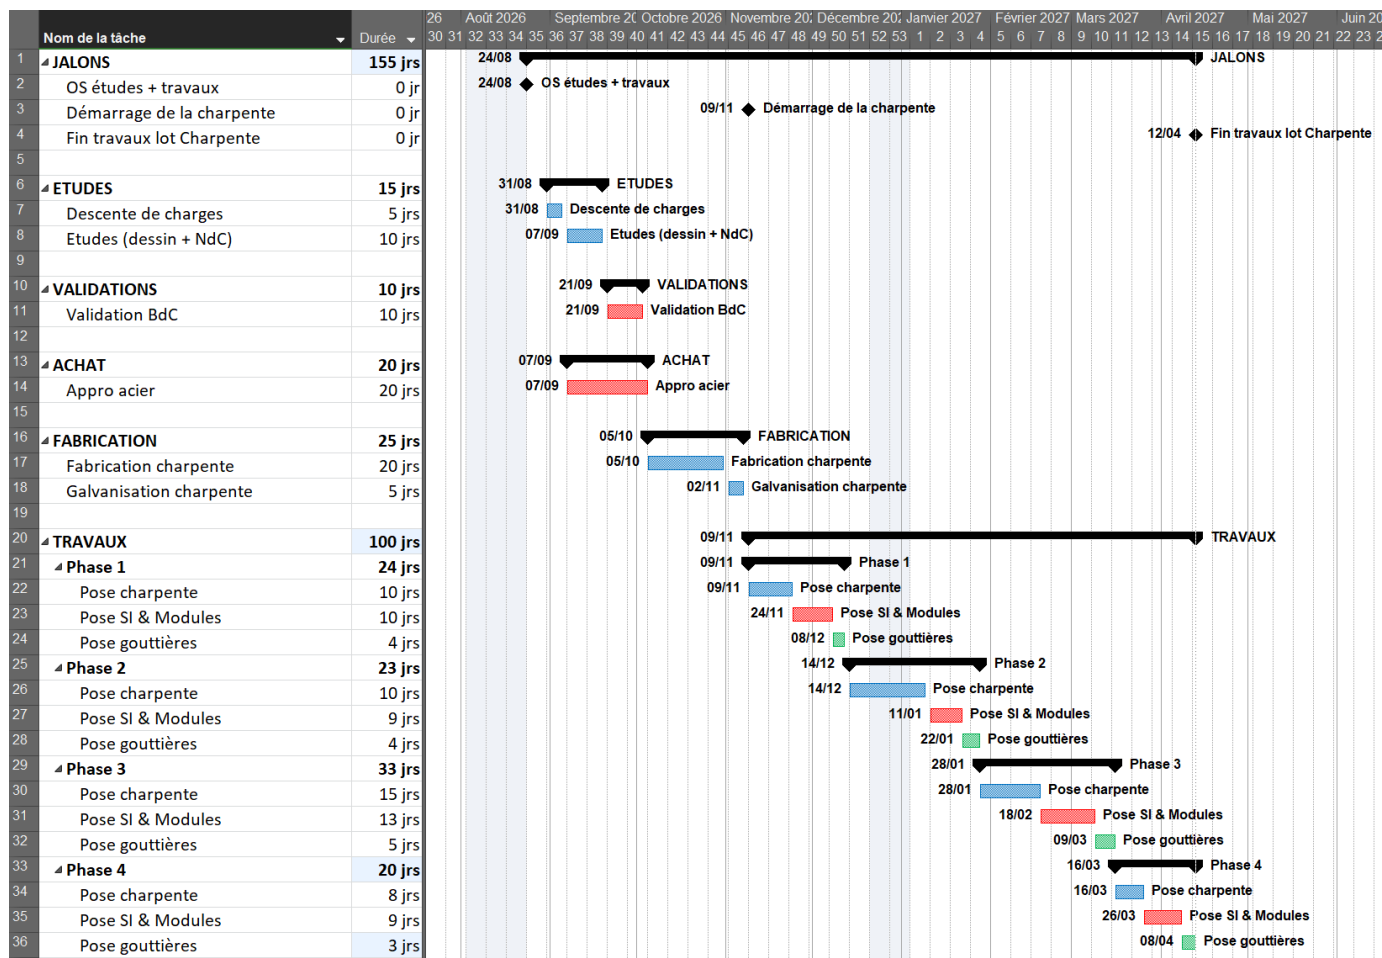

3. Hypothèses de calcul EUROCODES (OMBRIERE)

Chargements (suivant EN 1991 + AN) :

- Charges permanentes (G) :

- Poids propre de la charpente.
- Panneau photovoltaïque + système d'intégration : 18 daN/m²
- Divers : 2 daN/m²

- Neige (S) suivant EN 1991-1-3 + AN :

- région C1
- altitude 322m

- Vent (W) suivant EN 1991-1-4 + AN :

- région : 2
- rugosité : IIlb

- Actions accidentelles :

- Séisme (E) suivant EN 1998 + AN :

- Pour une installation disposée au-dessus d'un parc de stationnement disposé au niveau du sol, une ombrière ne constitue pas un bâtiment et n'est donc pas visé par arrêté du 22 octobre 2010. Il n'est donc pas nécessaire, pour la structure métallique, d'effectuer un dimensionnement et une vérification parasismique. De la même manière, la justification parasismique des panneaux photovoltaïques n'est pas requise.
- Choc de véhicule : il n'est pas prévu d'action accidentelle liée à un choc de véhicule.

Combinaison d'actions suivant EN 1990 + AN

Déformations suivant EN 1993 :

- Déplacements horizontaux en tête de poteaux limités au 1/100 de la hauteur sous combinaisons ELS.
- Flèche verticale des pannes limitée au 1/200 de la portée sous combinaisons ELS
- Flèche verticale des traverses limitée au 1/75 de la portée sous combinaisons ELS
- Flèche verticale des portes à faux limitée au 1/100 de la portée sous combinaisons ELS

Normes de dimensionnement :

- EN 1993 + AN
- EN 1994 + AN : calcul des structures mixtes acier-béton.
- RECOMMANDATIONS POUR L'APPLICATION DE LA NF EN 1991-1-4 AUX CHARPENTES ET OSSATURES EN ACIER DE BATIMENT - JUILLET 2017

Classe d'exécution : EXC2

Matériaux utilisés (sauf contre-indication précisée dans la note de calculs) :

- Acier de la structure métallique :
 - S275 pour les poutrelles du commerce type IPE, UPN, cornières.
 - S355 pour les PRS.
 - S235 pour le reste de la structure.

Nota :

Les profils formés à froid « PLS » sont calculés selon l'Eurocode EN 1993-1-3.

La méthode de calcul et le logiciel de calcul spécifique « Alouette 3.0 » ont été soumis au CTICM (Centre Technique Industriel de la Construction Métallique) qui a émis un avis favorable à l'utilisation de ce logiciel.

4. Documents utilisés pour l'étude :

Nom	Modifié le
 rebut	16/02/2024 16:21
 D_26_1027_IMPL_0001_A_Super_U_Exincourt.pdf	11/03/2026 16:03
 Super U Exincourt - Outil Dimensionnement RS-PARK 2.xlsx	11/03/2026 16:03

5. Suivi des modifications du devis

Indice A : Origine



Super_U_Exincourt

4 Rue Philippe Goudey
25400 Exincourt

TABEAU	Données du système d'intégration	Page	1
PLAN(S)	Plan de masse et plans Sud & Nord	Page(s)	02 à 04
COUPE(S)	Coupes ombrière 7 - 8 panneaux et liaisonnement	Page(s)	05 à 08
IMAGE(S)		Page(s)	

A	13/03/26	Première diffusion	DA	BT
B	24/03/26	Mise à jour	DA	BT
REV	DATE	NATURE DE LA MODIFICATION	Etabli par	Vérifié par
EMETTEUR	N°DEVIS	NUMERO DU DOCUMENT	PAGE	
BCM	50588		00	

ENTECH - Super_U_Exincourt

N° devis	50588
Adresse	4 Rue Philippe Goudey
	25400 Exincourt

Type de panneaux	DM465G12RT-B48HBW						
Sad ?	NON	ALTITUDE (m)	322	Zone Neige	C1	VENT	2
Dimension	Portrait	Longueur (mm)	1762	Largeur (mm)	1134	Épaisseur (mm)	30
Puissance (W)	465						
Pente en °	Degré :	6	Rugosité	IIIb			

SYSTEME D'INTEGRATION	JORISOLAR
------------------------------	------------------

N° Ombrière	Qté	Nbr. Lignes	Nbr. Colonnes	Qt modules	Emprise au sol	Puissance	Basse goutte (mm)	Htr sous bracon
1	1	7	37	259	525,48	120435	3500	2200
2	1	7	47	329	666,71	152985	3500	2200
3	1	8	32	256	519,63	119040	3500	2200
4	1	8	47	376	761,62	174840	3500	2200
5	1	7	11	77	158,30	35805	3500	2200
6	1	7	20	140	285,40	65100	3500	2200
7	1	7	11	77	158,30	35805	3500	2200
8	1	7	20	140	285,40	65100	3500	2200
9	1	7	11	77	158,30	35805	3500	2200
10	1	7	20	140	285,40	65100	3500	2200
11	1	7	11	77	158,30	35805	3500	2200
12	1	7	20	140	285,40	65100	3500	2200
13	1	7	37	259	525,48	120435	3500	2200
14	1	7	20	140	285,40	65100	3500	2200
15	1	7	37	259	525,48	120435	3500	2200
16	1	7	20	140	285,40	65100	3500	2200
17	1	7	37	259	525,48	120435	3500	2200
18	1	7	20	140	285,40	65100	3500	2200
19	1	7	35	245	497,24	113925	3500	2200
20	1	7	20	140	285,40	65100	3500	2200
21	1	7	33	231	468,99	107415	3500	2200
22	1	7	72	504	1019,76	234360	3500	2200
23	1	7	72	504	1019,76	234360	3500	2200
				0	0,00	0		
				4909	9972,08 m²	2282,69 kWc		



TABLEAU RECAPITULATIF	
SYSTEME	Jorisolar V2
TYPE DE MODULE	DM465G12RT-B48HBW
DIMENSION DE PANNEAU	1762 x 1134 ép. 30mm
SURFACE COUVERTE	9 972.08 m²
PUISSANCE	2 282.69 kWc
Nombre de modules	4 909


"Nos pannes réalisées en profilés minces formés à froid peuvent être d'épaisseur 1,5mm"



Liaisons

non
structurelle

"Nos pannes réalisées en profilés minces formés à froid peuvent être d'épaisseur 1,5mm"

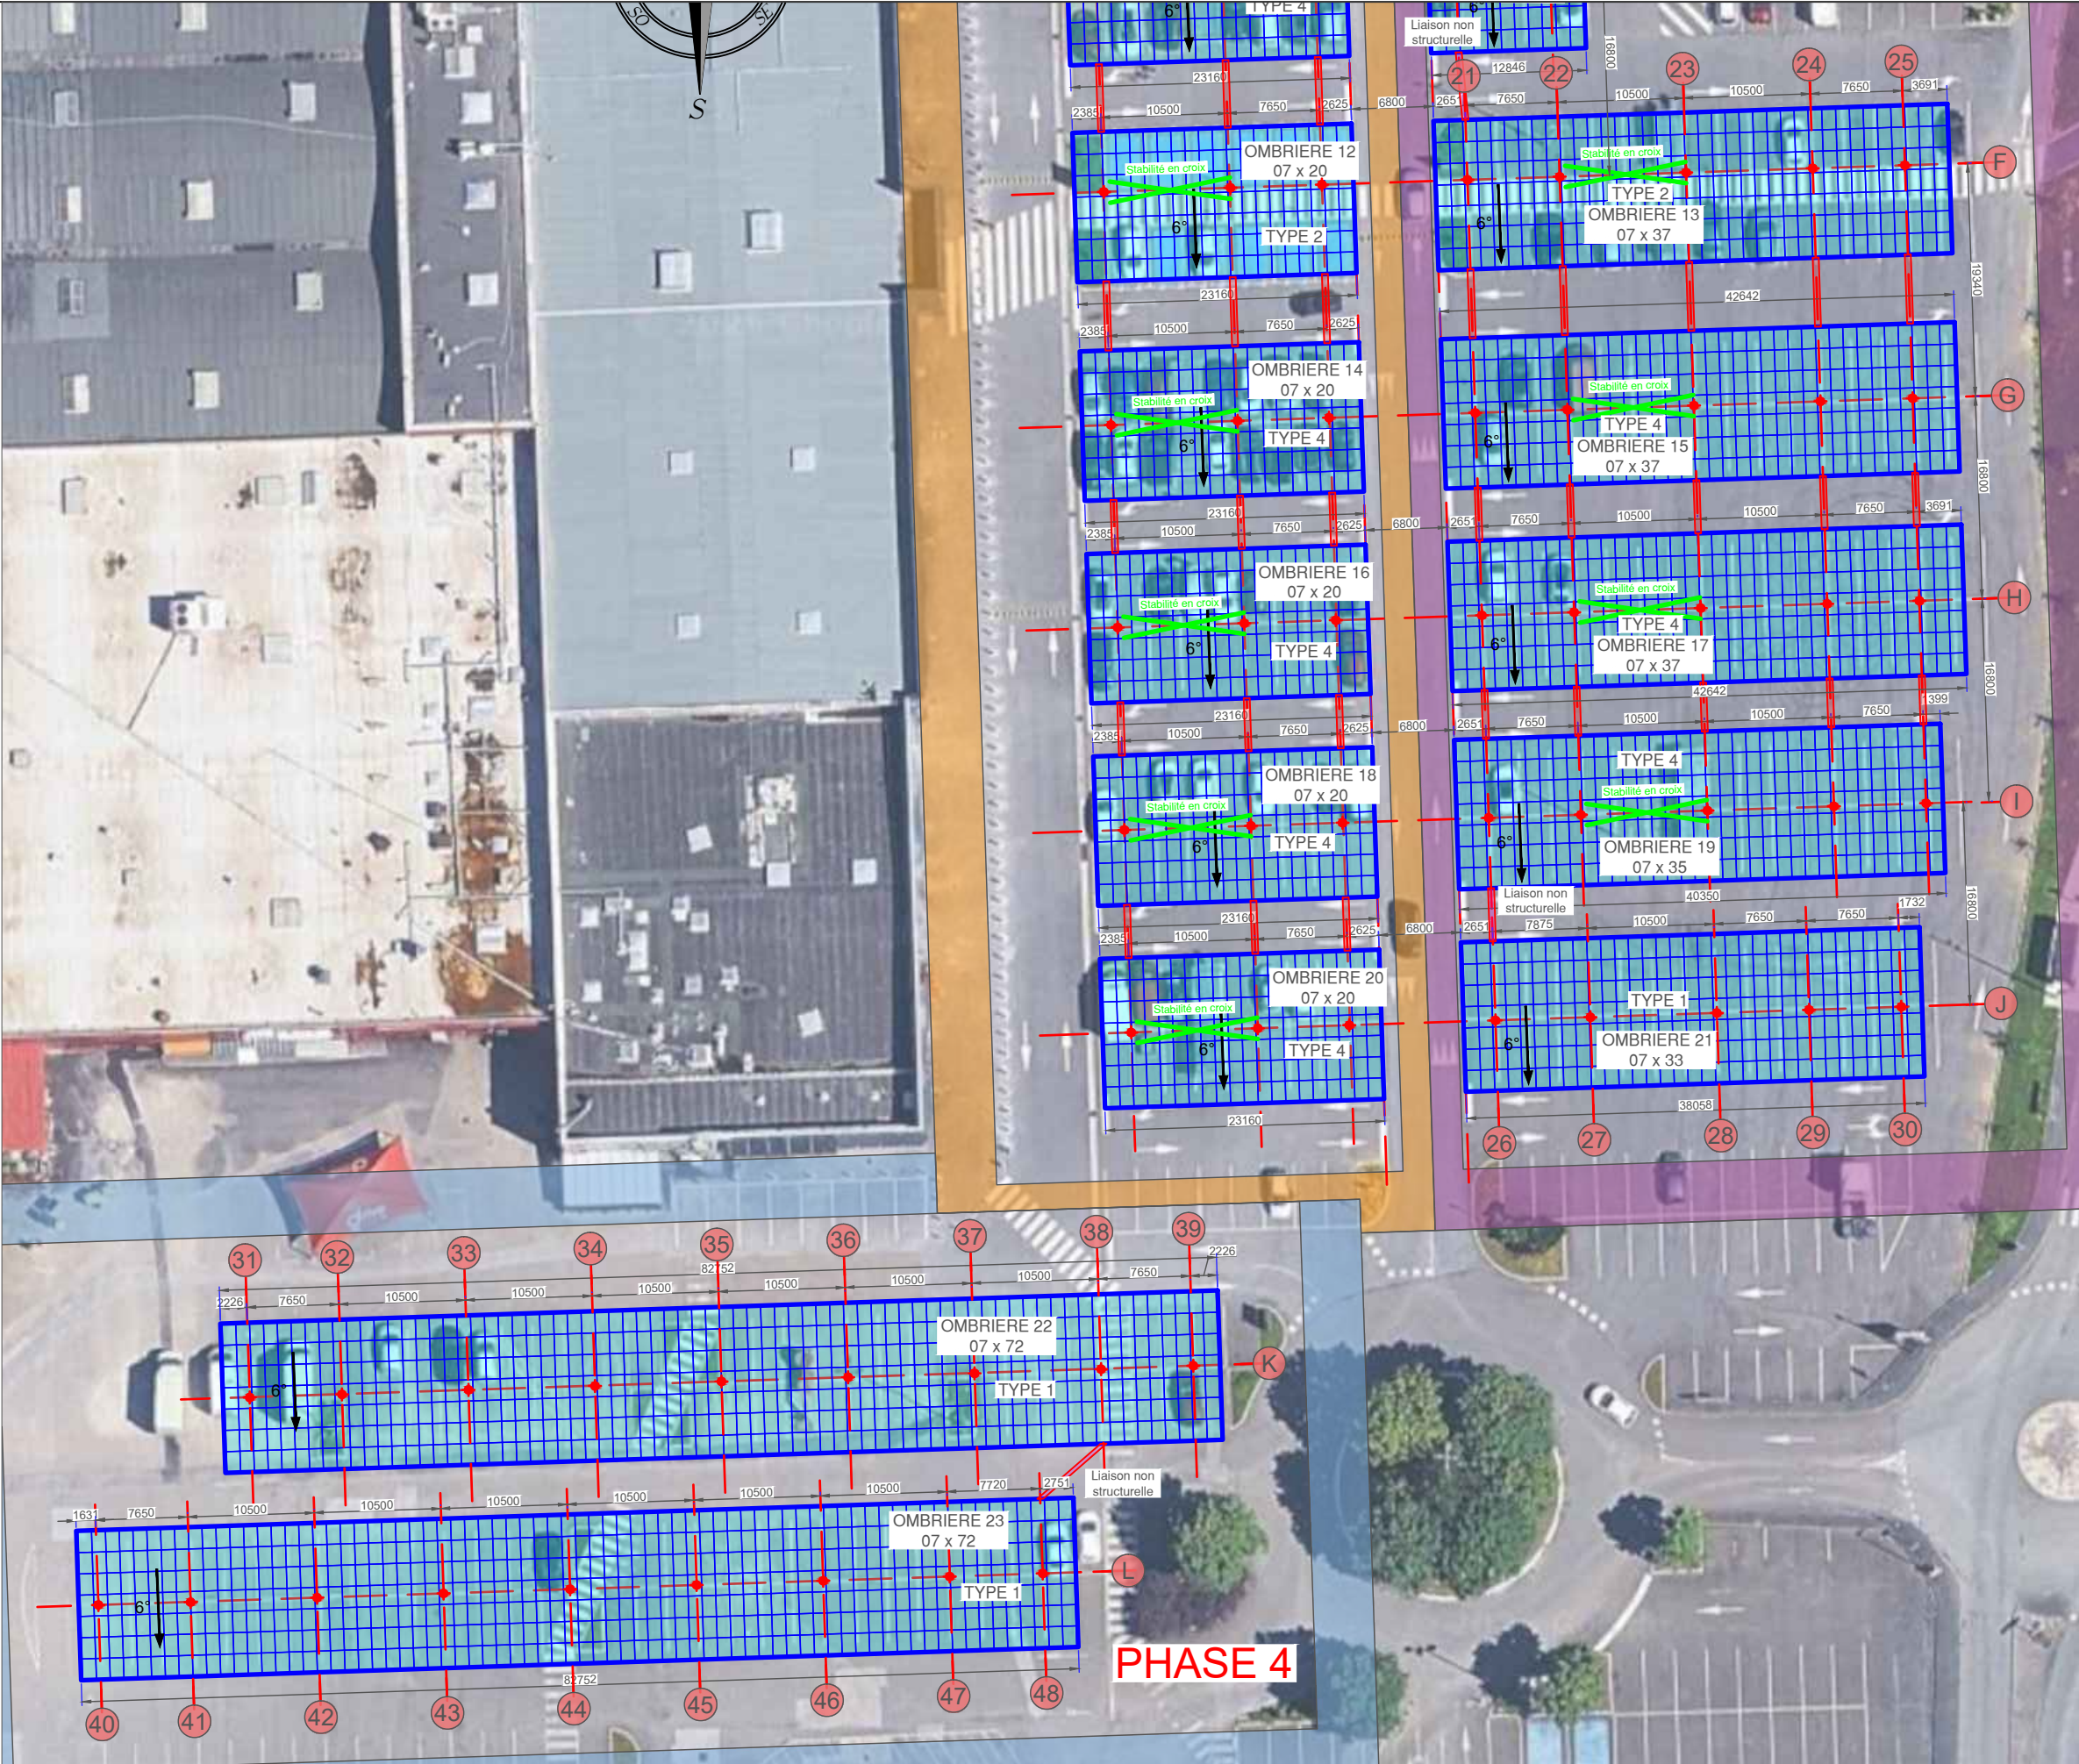


Liaisons




non
structurelle




"Nos pannes réalisées en profilés minces formés à froid peuvent être d'épaisseur 1,5mm"

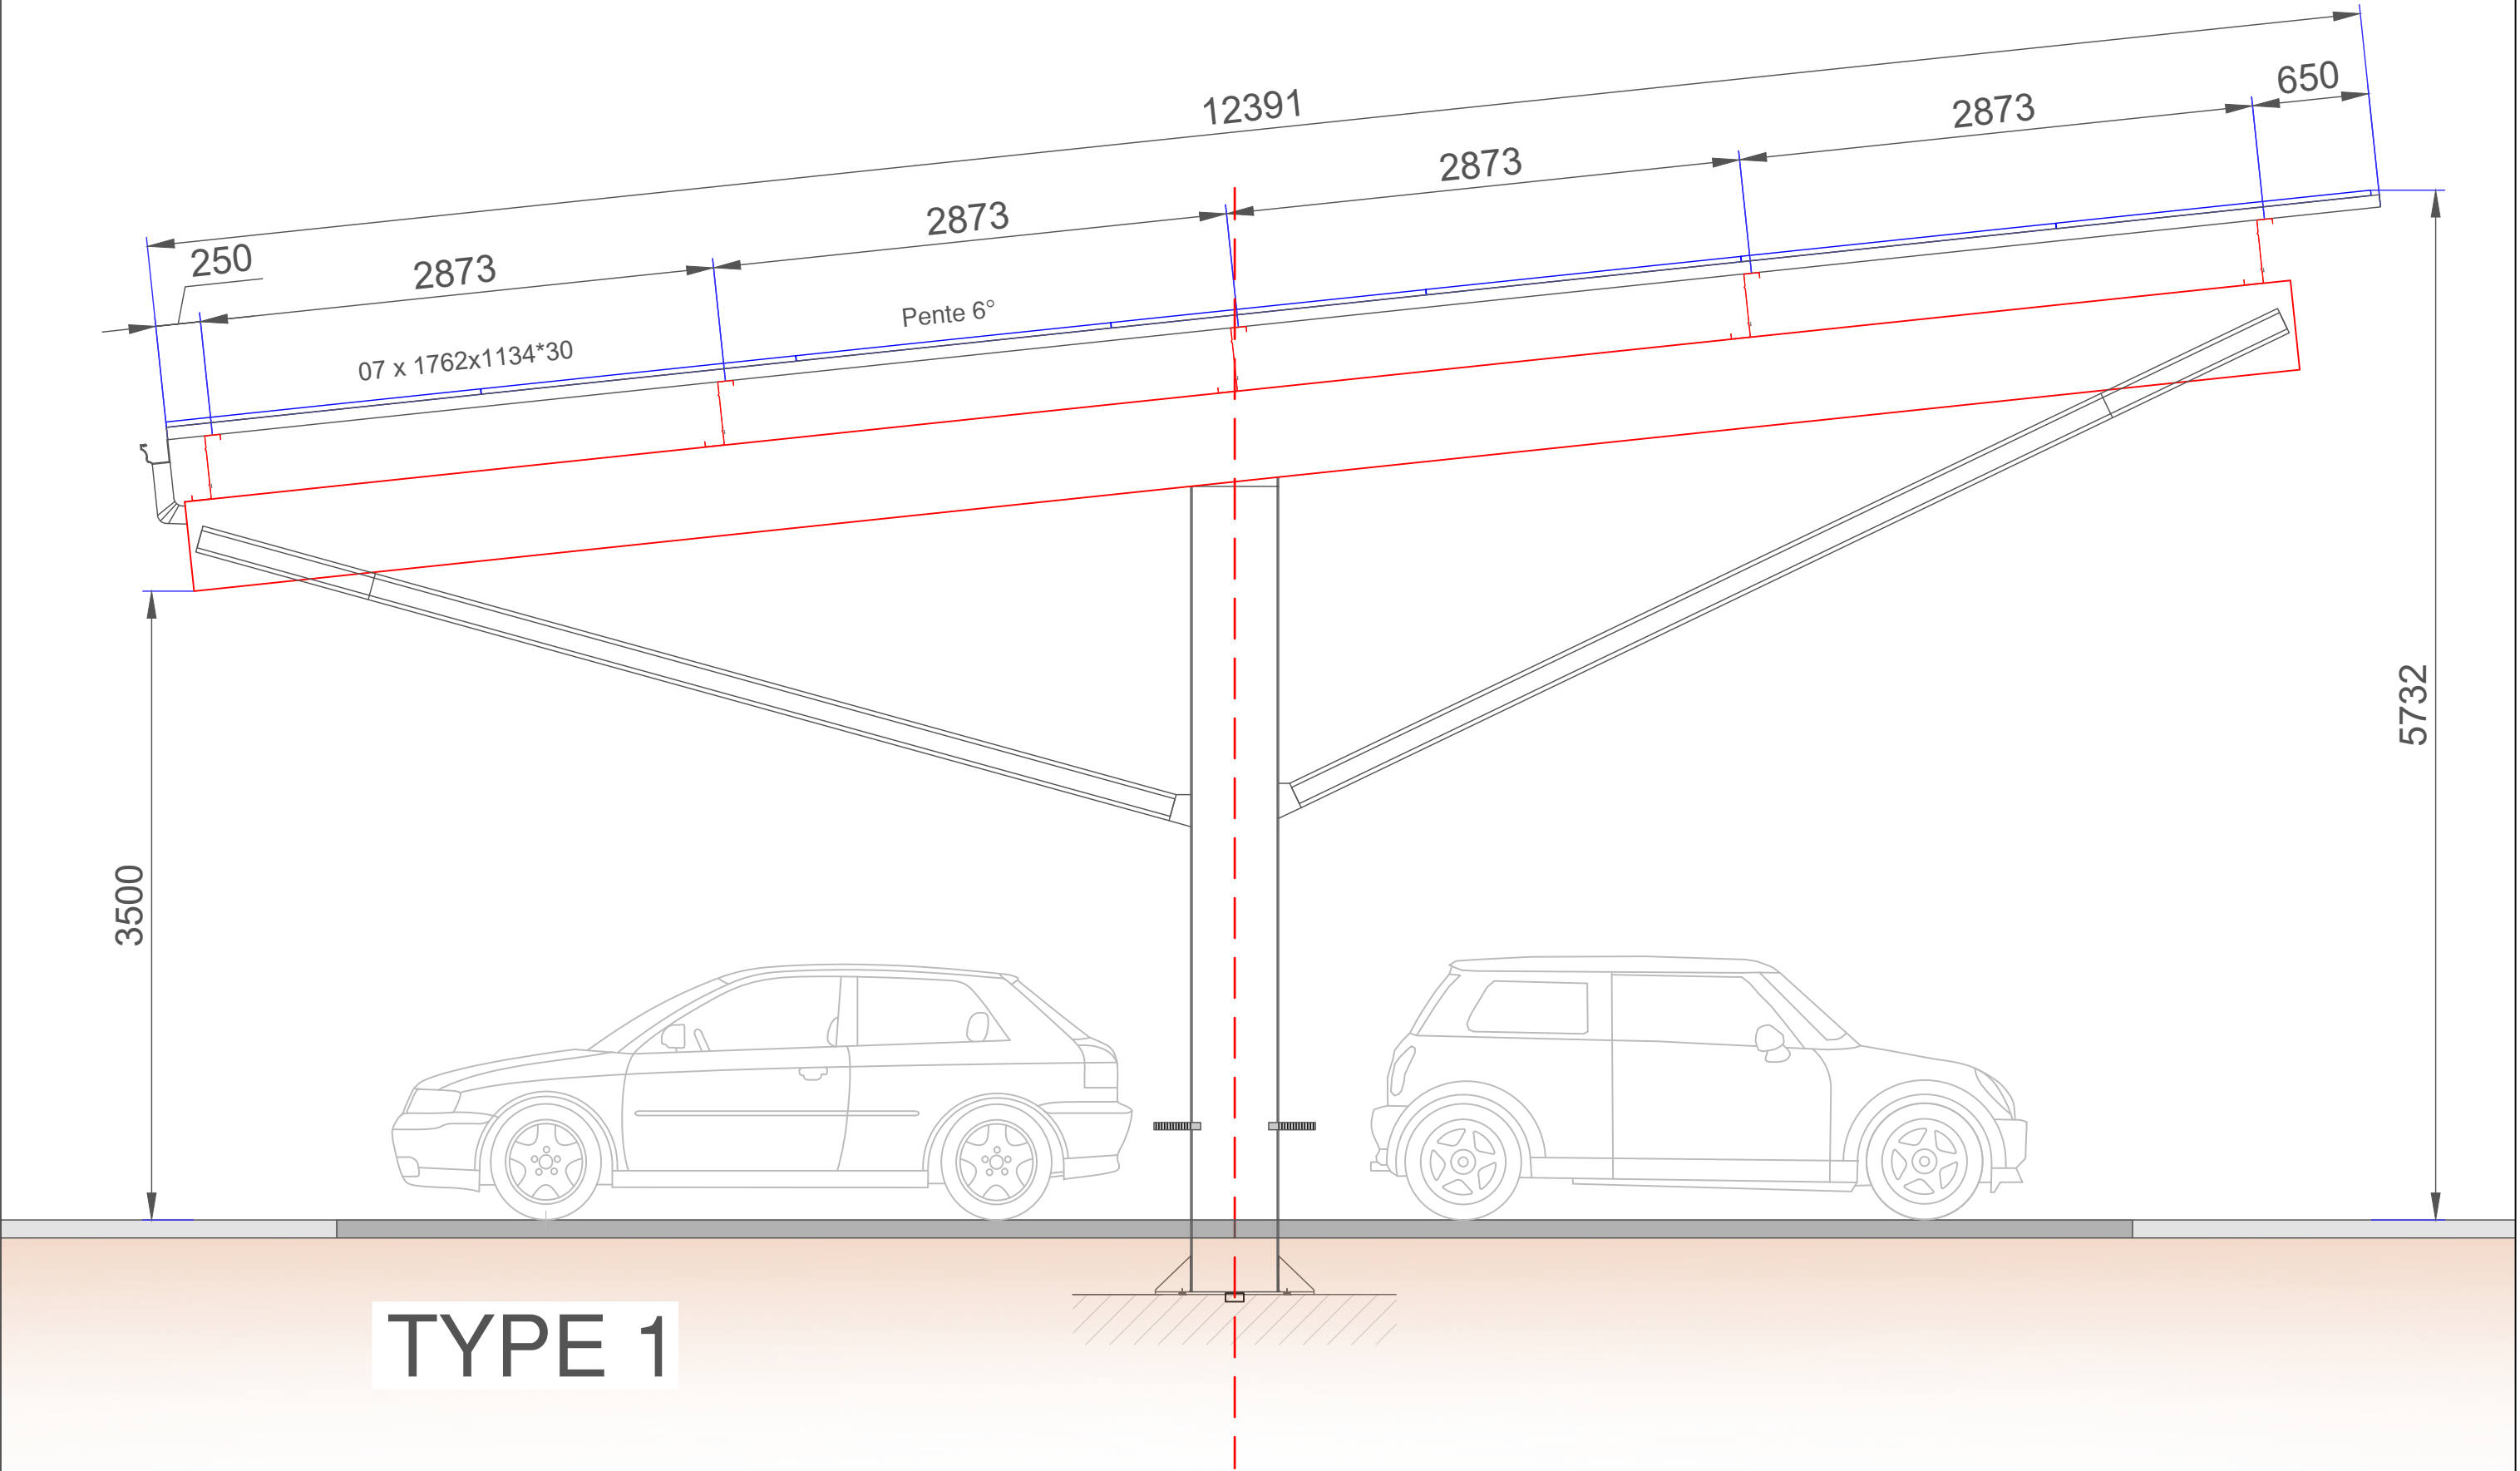

TYPE 1

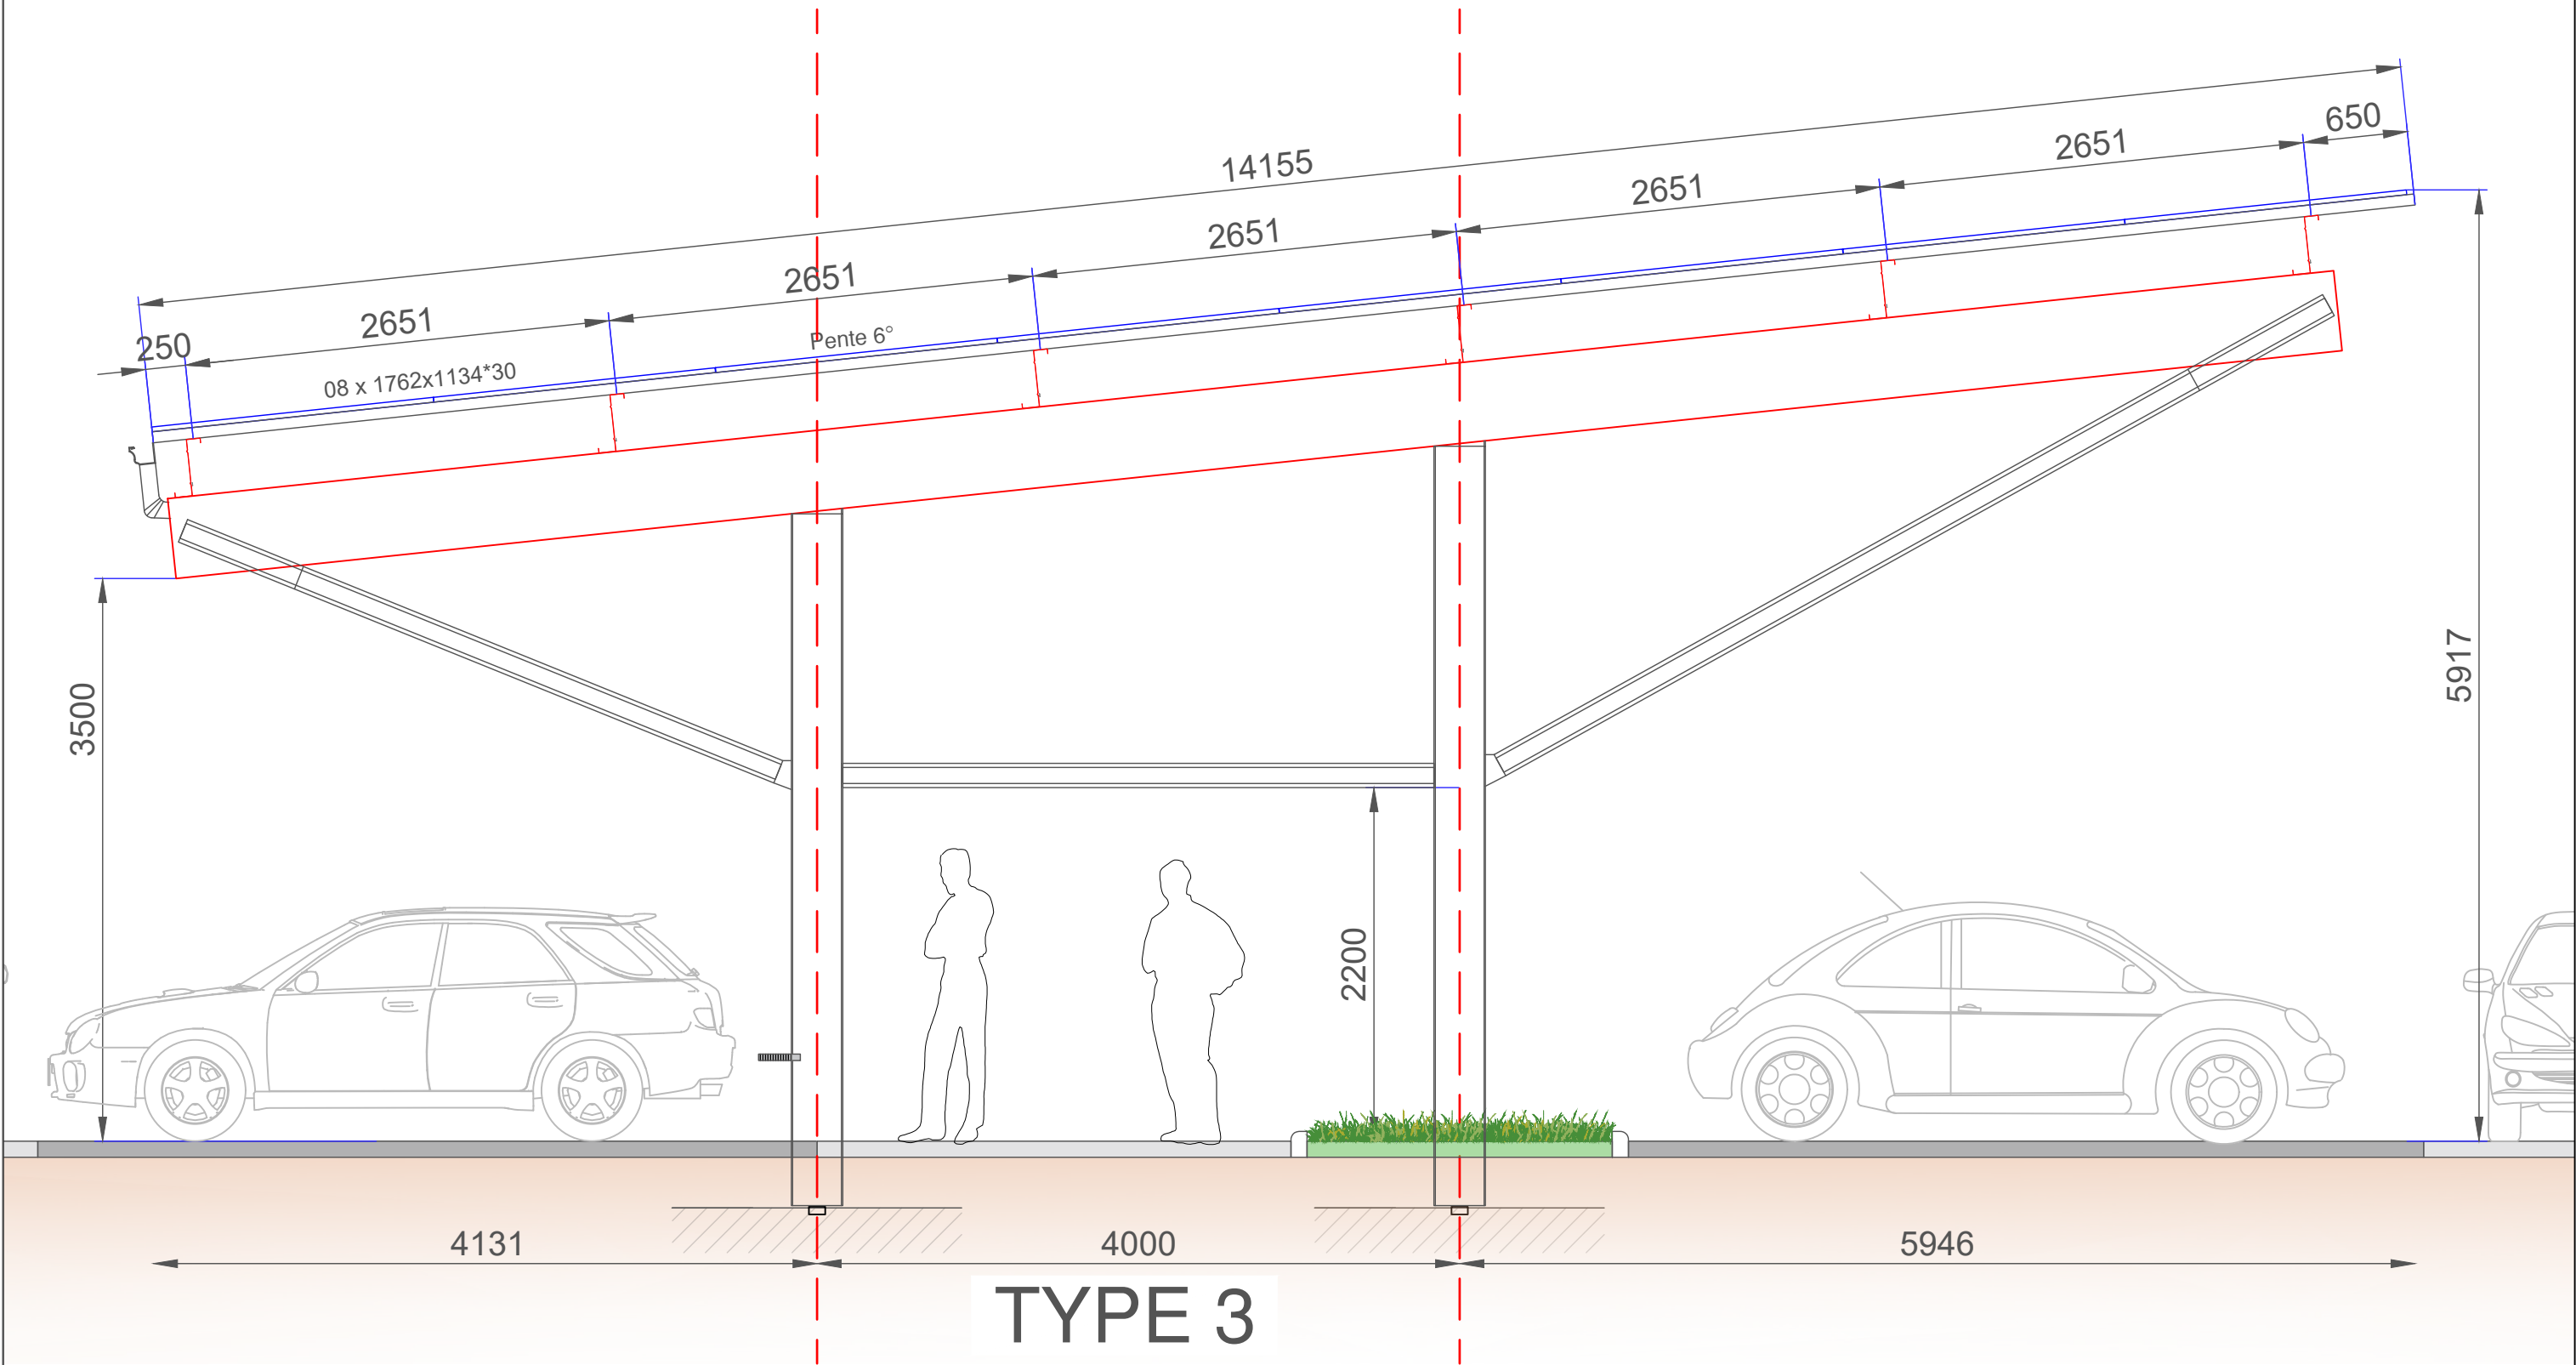

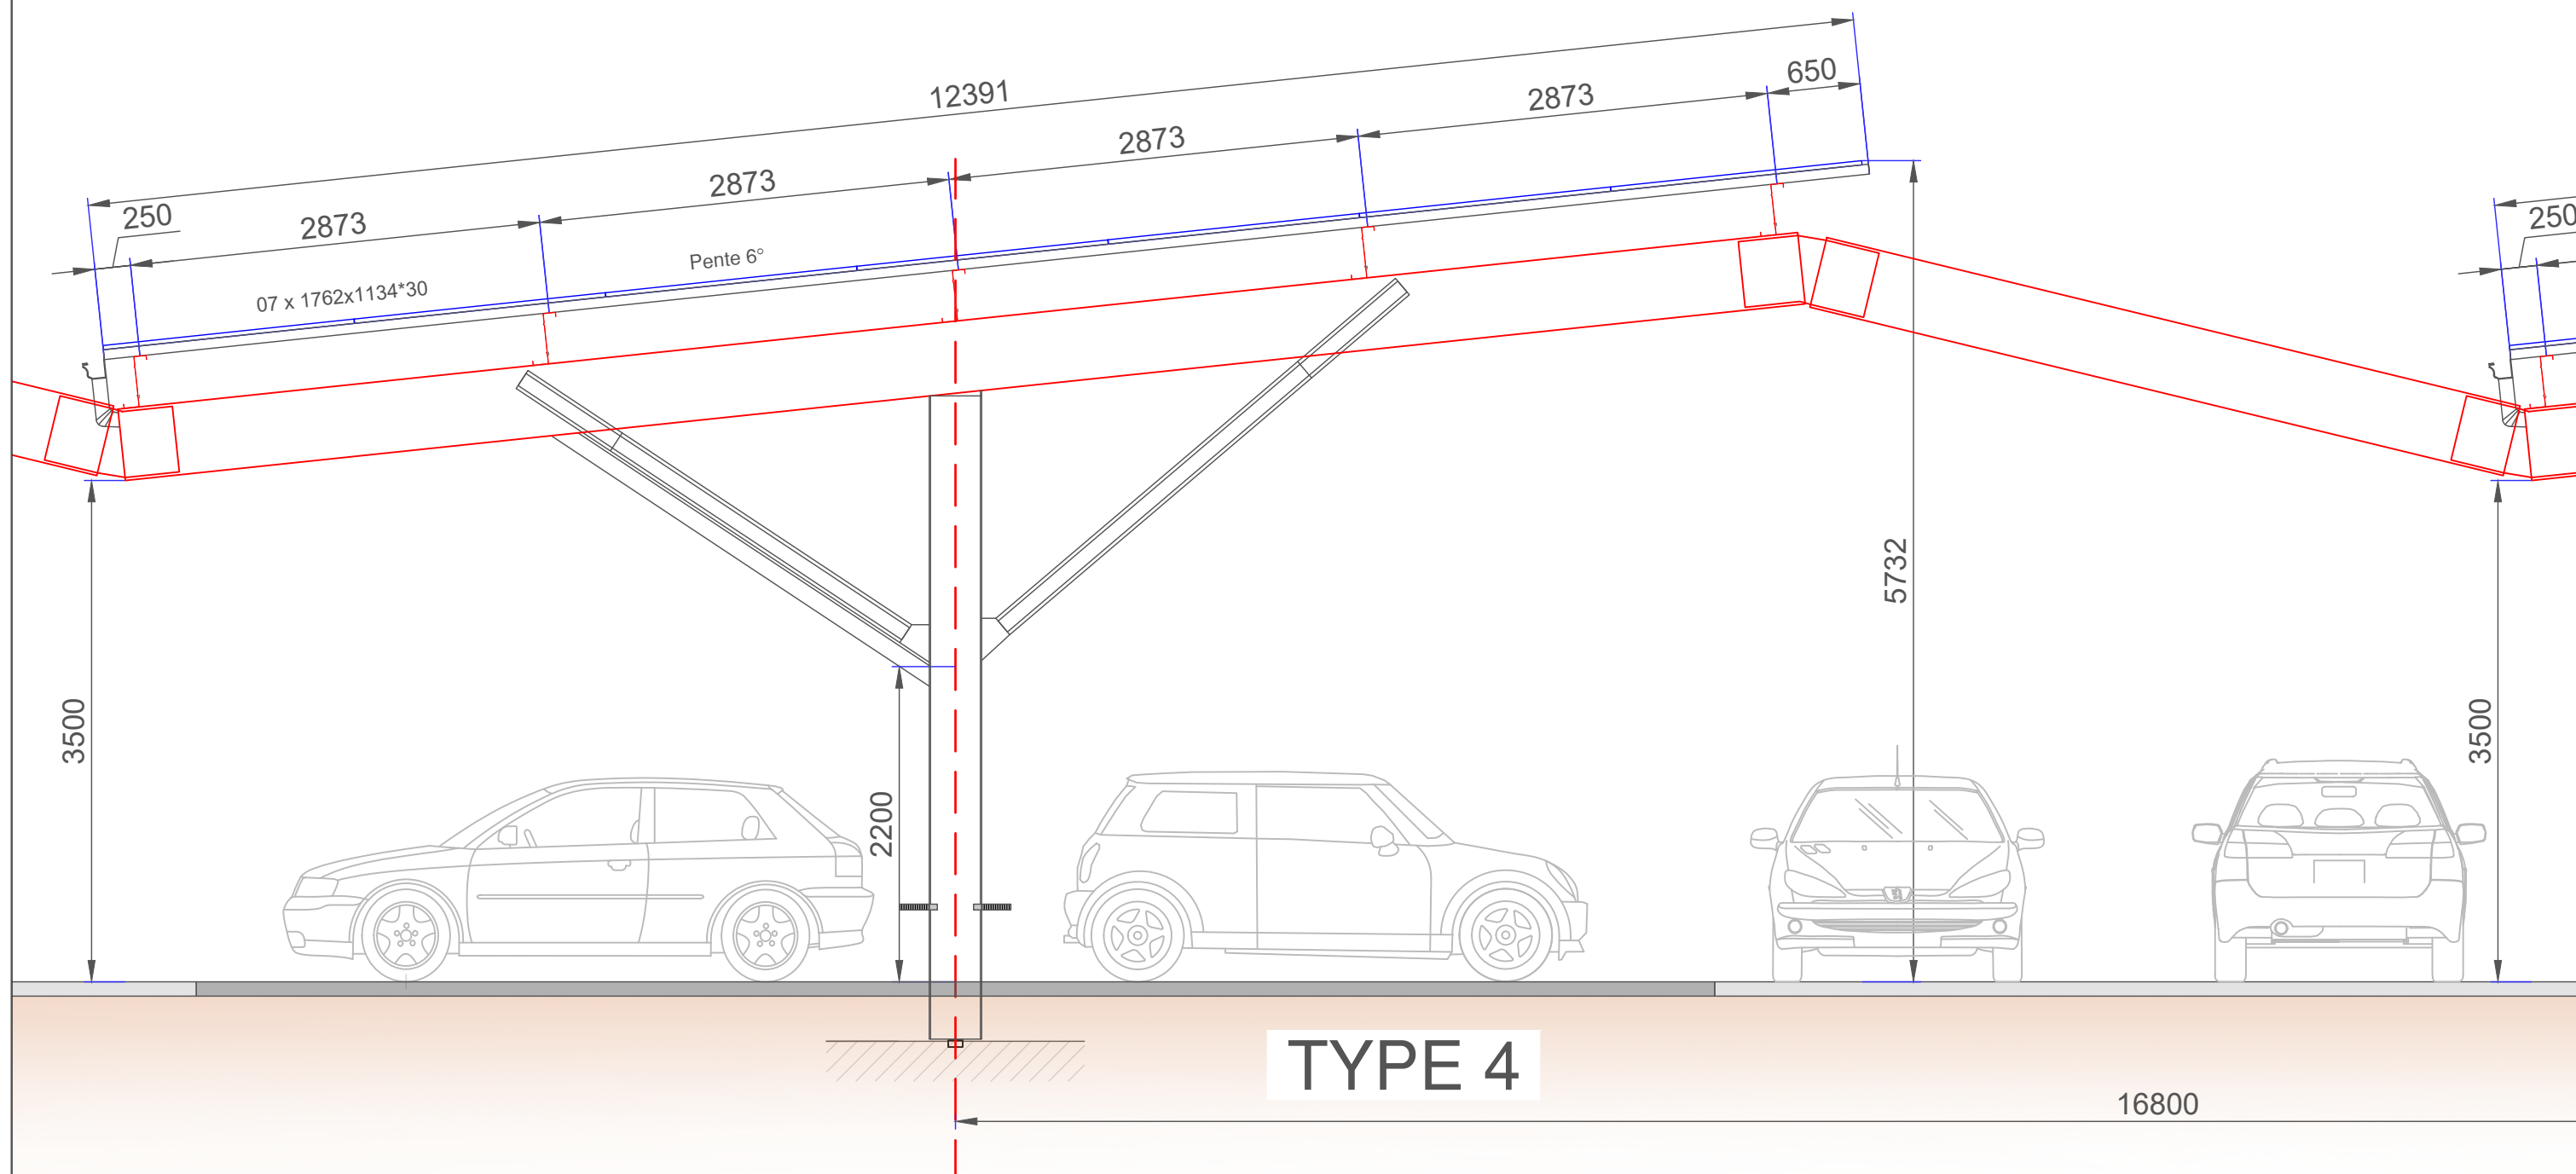

Description	Quantité	U	Prix unitaire	Prix total
<u>Ossature métallique ombrières</u>				
<i>Barrierage de chantier NON COMPRIS</i>				
Ossature métallique ombrière galvanisée	1	ens	548 833,54 €	548 833,54 €
Support onduleurs Composé de deux profilés minces formés à froid Ensemble boulonné sur poteau de structure Protection par galvanisation	9	U	54,00 €	486,00 €
Protection périphérique des poteaux constituée de deux arceaux métalliques galvanisés à chaud fixation sur poteau par crapeautage	192	U	57,00 €	10 944,00 €
Capotage des descentes de câble Toile acier galvanisé au droit du poteau	9	u	130,78 €	1 177,02 €
Liaison non structurelle entre ombrière constituée de un profil mince formé à froid pour support de chemin de câble	5	U	253,00 €	1 265,00 €
<u>Gestion des E.P.</u>				
Gouttière alu (compris les naissances, jonction, fonds, crochets ...)	796	ml	93,20 €	74 187,20 €
<u>Système d'intégration et modules PV</u>				
Fourniture du système d'intégration de type JorisIde RS Park fixation sur panne par boulon en fond de rail sous réserve de compatibilité avec les modules PV	4909	U	27,70 €	135 979,30 €
Pose du système d'intégration et panneaux dim. 1,762m x 1,134m suivant système Jorisolar RS PARK	9809	m²	9,32 €	91 397,57 €
Total H.T.				864 269,63 €

Nos prix sont établis en tenant compte de la mise à disposition d'une plate-forme stable non boueuse, de massifs et de pieds de mur remblayés (en cas de longrine ou murs préfabriqués), permettant l'évolution des engins de levage en sécurité (grue, nacelle ...) sur la totalité de l'aire de montage.

Dans le cas contraire, nous ne pourrions être tenus pour responsables d'un retard ou d'un arrêt de l'exécution de nos travaux, ainsi que d'éventuelles salissures de boue sur l'ossature métallique.

Ne sont pas compris dans notre fourniture :

- Les scellements et trous de scellements ainsi que tous travaux de maçonnerie quels qu'ils soient.
- Les accès au chantier, les plates-formes de circulation à l'intérieur du chantier.
- La fourniture de courant électrique.
- L'isolation éventuelle d'une ligne électrique et les dispositions relatives à la mise hors tension éventuelle d'une ligne électrique, basse, moyenne ou haute tension.
- La mise à la terre.

Nous attirons votre attention sur les différences d'aspects qui ne manqueront pas d'apparaître sur les éléments galvanisés. Sur un même élément, des parties pourront être mates, grises ou brillantes. Ces modifications d'aspect sont dues aux différences des teneurs en silicium entrant dans la composition de l'acier traité, et n'altèrent en rien la qualité de la galvanisation. Nous ne pouvons être tenus pour responsables de ces différences d'aspects.

ÉTUDES ET PROJETS - Les études et projets de toute nature, remis ou envoyés par BRIAND CONSTRUCTION METALLIQUE restent toujours sa propriété. Sur sa demande ils peuvent être rendus. BRIAND CONSTRUCTION METALLIQUE conserve intégralement la propriété intellectuelle de ses projets qui ne peuvent être communiqués ni exécutés sans une autorisation écrite.

CONDITIONS DE VENTE - Nos fournitures sont considérées comme traitées et payables aux Herbiers, sans dérogation possible à cette clause attributive de juridiction. Les commandes faites à nos représentants ne nous engagent qu'après acceptation de notre part. Nos représentants n'ont pas qualité pour encaisser les fonds à valoir sur les commandes. Les travaux non prévus dans nos devis ou forfaits ne peuvent en aucun cas être à notre charge. Les délais sont donnés à titre indicatif, le retard ne peut en aucun cas être invoqué comme cause d'annulation de la commande, et il ne donne droit à aucune indemnité, sauf convention expresse.

En l'absence de dispositions particulières contraires, la norme AFNOR NF P 03-001, de décembre 2000, vaut pièce contractuelle complémentaire.

CONDITIONS DE PAIEMENT - Nos prix s'entendent pour paiement comptant. Le fait d'accepter un règlement par traite à échéance ne fait pas dérogation à cette clause. Ils sont nets et sans escompte.

RETARD OU DÉFAUT DE PAIEMENT - De convention expresse et sauf report accordé par nous, tout dépassement de l'échéance initiale sera passible de plein droit (art. L 441-6 du Code de Commerce) d'intérêts équivalents à trois fois le taux légal en vigueur. Ces pénalités sont exigibles dès le lendemain de la date de règlement figurant sur la facture. De plus, à titre de dommages et intérêts, une indemnité légale à 15% de la somme impayée sera appliquée ainsi que les frais judiciaires. Le défaut de paiement pour quelque cause que ce soit nous autorise à interrompre immédiatement les travaux et à considérer le marché comme étant résilié sans qu'il soit besoin d'aucune mise en demeure ou formalité judiciaire, tous droits à dommages et intérêts étant réservés pour nous.

Toutes nos opérations relèvent de la compétence du Tribunal de Commerce de la Roche sur Yon.

Nous nous réservons la possibilité d'utiliser la photographie des travaux réalisés à titre de référence et pour notre publicité.

TRANSFERT DE PROPRIÉTÉ - Le transfert de propriété est suspendu au paiement effectif et intégral du prix défini.

BRIAND CONSTRUCTION METALLIQUE

Le 24/03/2026

Paraphe, Signature précédée de la mention

"Bon pour accord"

ENTECH

Le / /

Paraphe, Signature précédée de la mention

"Bon pour accord"



Briand Construction Métallique

21 rue André Lwoff
69800 Saint-Priest
Tél : 04 78 70 80 49

briandmetal.fr