

SIMASTOCK
LAMBRES - LEZ-DOUAI

COUPE D - D
1:25

1*

4 Cheilles SPIT FIX III - M12*100

+14450

255 200 25

ACROTERE

30

50

+14450

350

400

TUBE-C-90*90*3

Découpe partielle
panneau largeur
80mm pour passage
de la chaise

jeu 70

chemin de
cables (13 kg/m)

penne 3%

panneaux laine de roche
31 VULCASTEEL ROOF
80-37-250
EI 60 mm

accessoires de finition
périphériques (3 cotés)
laqués 75/100e

2 plots réglables
par chaise

couverture
existante

4 Cheilles SPIT FIX III - M12*100


pannes métalliques galva
en tube

1*

Largeur 1700 - Longueur 8000 cellule 1

Largeur 1200 - Longueur 6000 cellules 2 à 8


chaises métalliques galva
reprises sur 2 lisses (90x90)

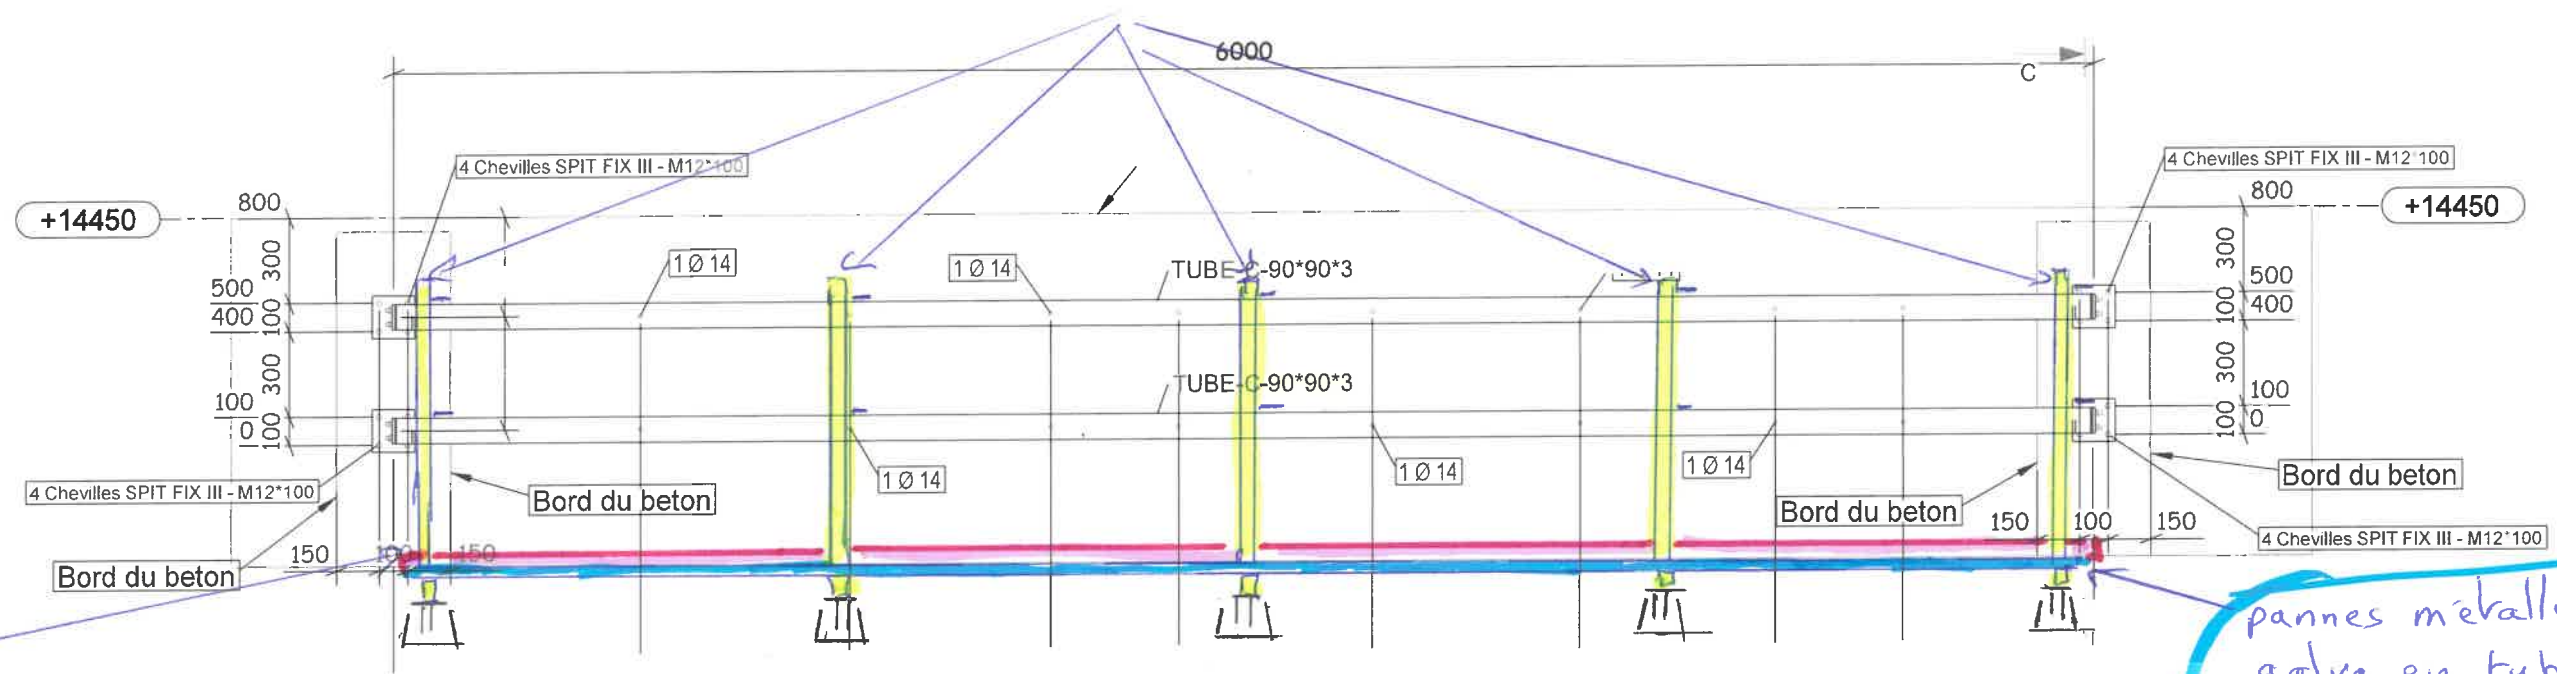

panneaux
long 1200
Cellules 2 à 8

pannes métalliques
galva en tube

Détail A
1:25

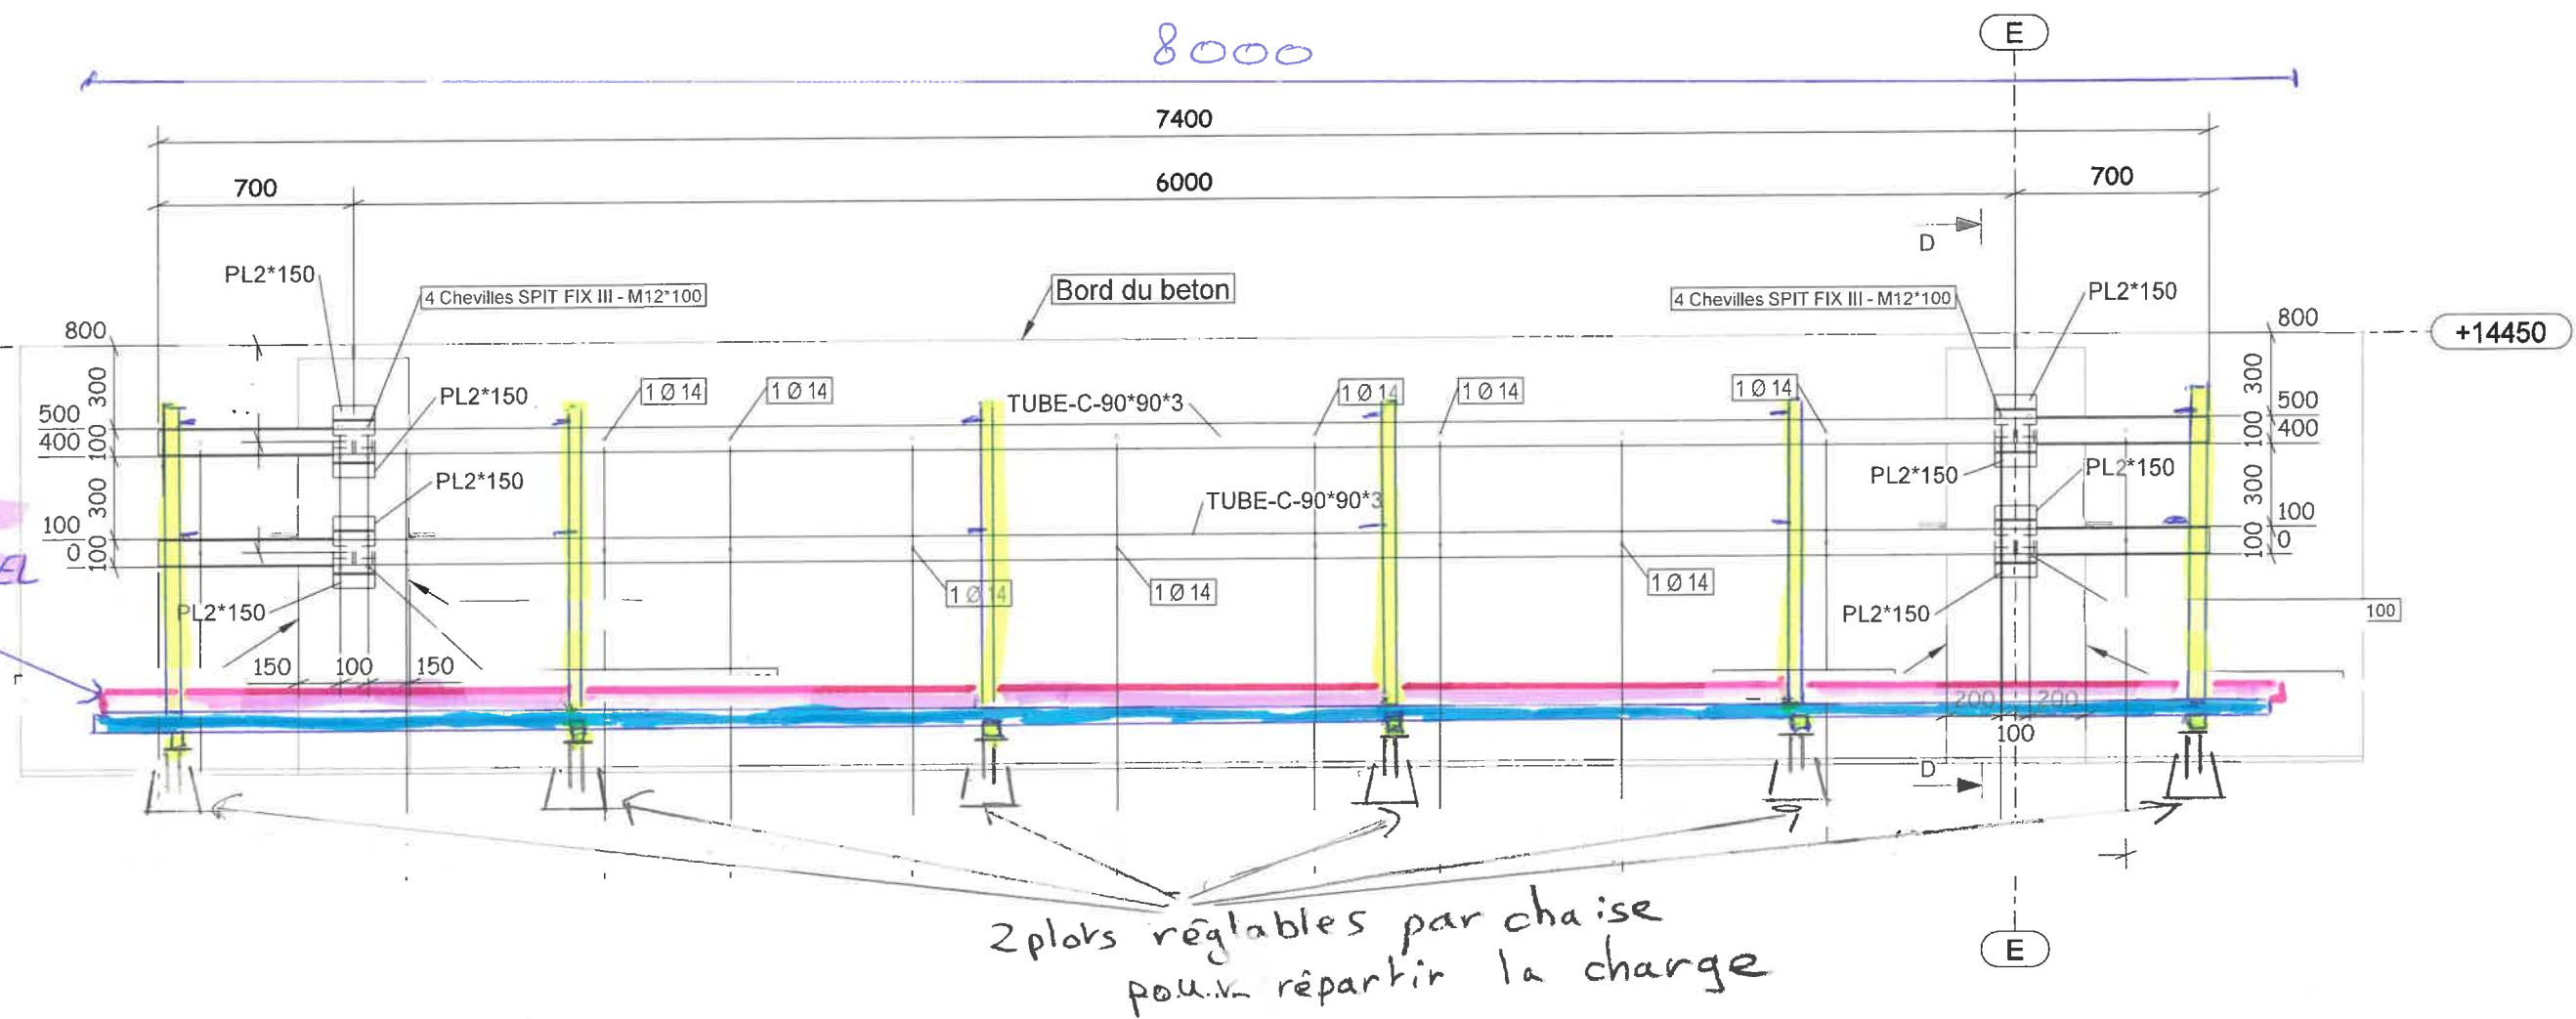

panneaux laine de
roche SI VULCASTEEL
ROOF EI 60mm
long 1700
cellule 1

2 plots réglables par chaise
pour répartir la charge

